


CONCEPT, NOT FOR FABRICATION


BankHaul · github.com/BoujeeEnjinia1701/bankhaul

REV	DESCRIPTION	DATE	BY
P1	Preliminary GA for TRL 3 (from cad/src/model.py)	2026-10-03	AC
P2	BKH-DDR-002: design for construction	2026-10-03	AC

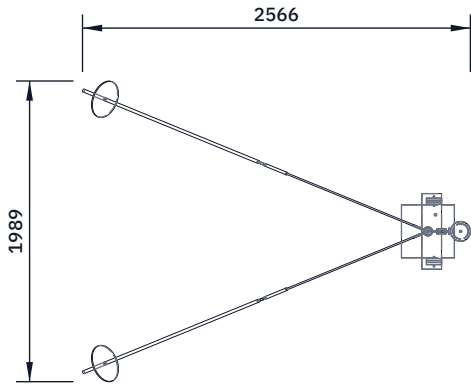


TOP VIEW

Scale 1:50; looking down (along -Z)

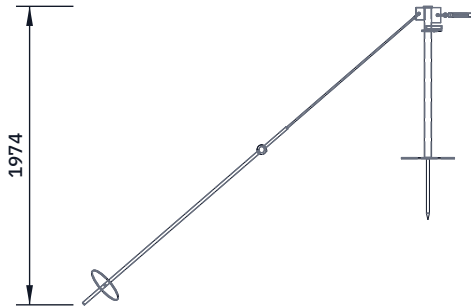


FRONT VIEW

Scale 1:50; looking at the front (along +Y)

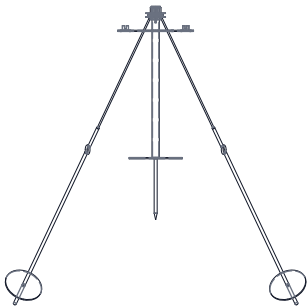

RIGHT VIEW

Scale 1:50; looking at the right side (along -X)

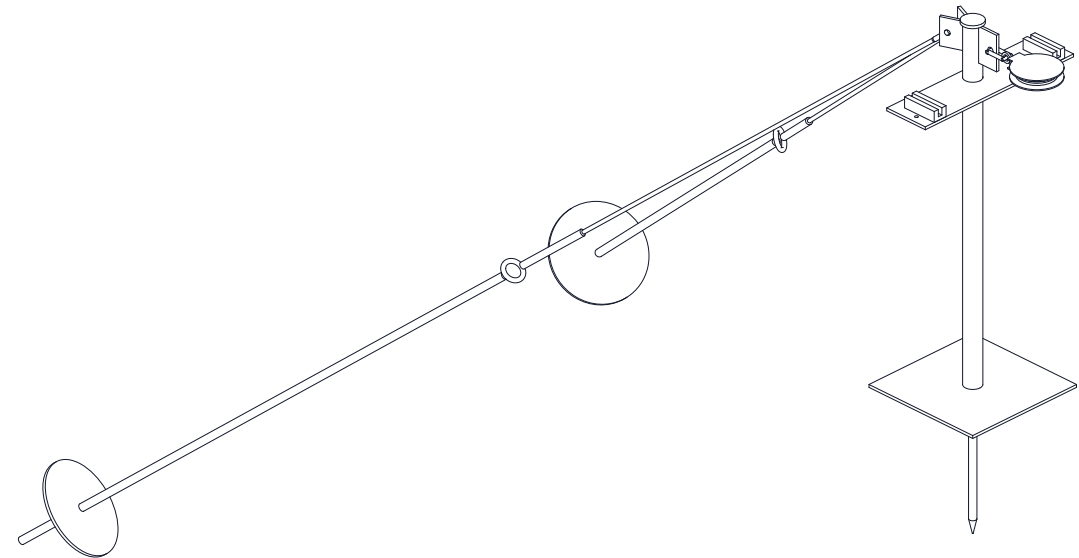

ISOMETRIC VIEW

Not to scale; ground at $z = 0$; seen from the front right and above, about 30 deg elevation

MAIN DIMENSIONS AND INTERFACES (MM)

Post 48.3 x 3.2 tube, head 1,000 above the ground; weldment 17.2 kg (1)

Foot plate 350 x 350 x 8; ground spike 20 round, 400 below the plate

Pad eye 18 hole 64 from the post axis, 950 up; near block on a shackle (8, 13)

Near sheave centre 216 in front of the post; legs 112 apart

Two stay lugs, 15 holes, 960 up, splayed 22.2 deg either side of the line

Back-stays 10 rope with M12 turnbuckles to the anchor eyes (5, 12)

Anchor eyes 1,100 behind and 450 either side; rods in line with the stays (11)

Cleat bar 130 x 500 x 8 slipped over the post, top 850 up; jam cleats 200 either side (10)

Tie-off hole 15 dia in the cleat bar for the net's near end

Third-angle; front view from -Y; the loop runs out to +X; (n) = BOM line

BANKHAUL

github.com/BoujeeEnjinia1701/bankhaul

Bank station: general arrangement

DRAWING NO.

BKH-DWG-001

REV

P2

SHEET

1 of 1

SIZE

ANSI B

SCALE

1:50

UNITS

mm

PROJECTION



DATE

2026-10-03

DRAWN

Amish Chadha

MATERIAL / NOTES

Steel weldment, bought blocks, anchors and rigging per bom/bom.csv. PRELIMINARY, NOT FOR FABRICATION

Licensed CERN-OHL-S-2.0 · Design Molecule Lab · designmolecule.com

Generated from cad/src; do not edit by hand