


CONCEPT, NOT FOR FABRICATION


BankHaul · github.com/BoujeeEnjinia1701/bankhaul

REV	DESCRIPTION	DATE	BY
P1	Preliminary GA for TRL 3 (from cad/src/model.py)	2026-10-03	AC
P2	BKH-DDR-002: design for construction	2026-10-03	AC

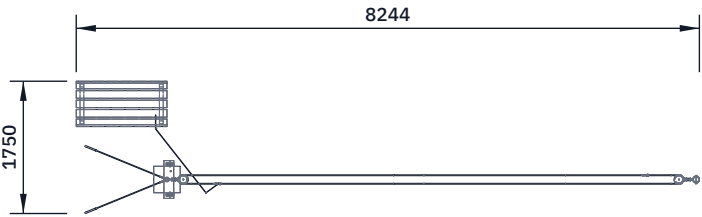


TOP VIEW

Scale 1:100; looking down (along -Z)

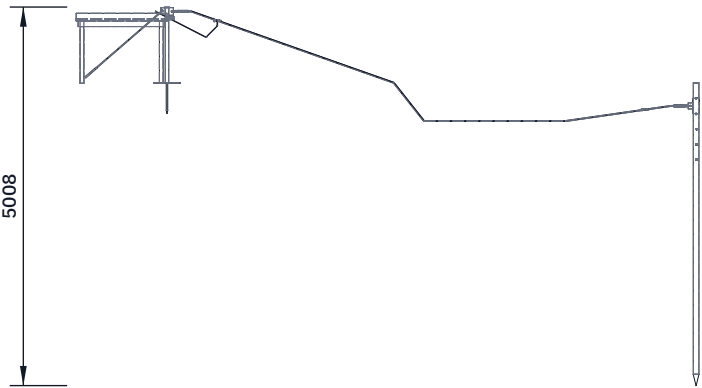

FRONT VIEW

Scale 1:100; looking at the front (along +Y)

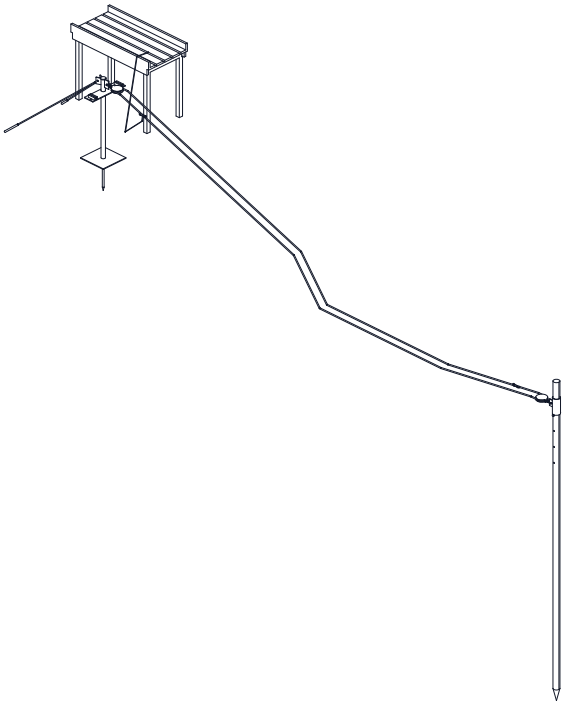

ISOMETRIC VIEW

Not to scale; span shortened to 7 m; seen from the front right and above, about 30 deg elevation

LAYOUT RULES (MM)

- Design span 30,000 between sheave centres; stretch 50,000 (R2)
- Post at least 6,000 back from the water's edge (R11)
- The fisher works within 1,000 of the post, never nearer the water
- Loop legs 112 apart, floating; the net is set along the -Y leg
- Net no longer than the span less 2,000, so no ring reaches a block
- Loop direction within the stays' splay (22 deg either side)
- Clearing table landward on the +Y side, clear of the stays
- Far stake set from a boat or at low water, never by wading
- Nobody in the bight of the loop or in line with a loaded stay
- Third-angle; front view from -Y; X along the loop

BANKHAUL

github.com/BoujeeEnjinia1701/bankhaul

Net-hauling station: layout (span shortened)

DRAWING NO. BKH-DWG-003			REV P2	SHEET 1 of 1	SIZE ANSI B
SCALE 1:100	UNITS mm	PROJECTION 	DATE 2026-10-03		DRAWN Amish Chadha
MATERIAL / NOTES Layout only; parts per BKH-DWG-001, 002 and 101 to 107. PRELIMINARY, NOT FOR FABRICATION					
Licensed CERN-OHL-S-2.0 · Design Molecule Lab · designmolecule.com				Generated from cad/src; do not edit by hand	